Отделочный план подвала Библиотеки на отм. -3.000



Условные обозначения

+7.500	-отметка уровня
1t	-марка пола
Д1	-марка двери
ОК-1	-марка окна
ПД-1	- подоконная доска
ВВ-1	- марка витража
холл	- наименование помещения
12.30	- площадь помещения

- Монолитный железобетон
- Керамический кирпич
- Газоблок
- Утеплитель



Количество комнат

- МОП
- Служеные помещения
- Техническое помещение

						1234 - ЭП-1	
						Многоквартирный жилой комплекс: «Многоквартирный жилой комплекс со встроенными помещениями и паркингом, III очередь строительства»	
Изм.	Кол.уч.	Лист	№док.	Подп.	Дата		
		Иванов А.				Стадия	Лист	Листов
						РП	0-1	
						Отделочный план подвала Библиотеки на отм. -3.000	Лого	

Взам. инв. №

Подп. и дата

Инв. № подл.

02.11.2026 14:56:10

Формат А2А

Отделочный план 1го этажа Библиотеки на отм. 0,000



Условные обозначения

+7.500	-отметка уровня
1t	-марка пола
Д1	-марка двери
ОК-1	-марка окна
ПД-1	- подоконная доска
ВВ-1	- марка витража
холл	- наименование помещения
12.30	- площадь помещения

- Монолитный железобетон
- Керамический кирпич
- Газоблок
- Утеплитель



Количество комнат

- Гардероб
- МОП
- С/у
- Служеные помещения
- Техническое помещение
- Читальная зона

Экспликация помещений 1го этажа...

Арендатор	Площадь
Гардероб	307,56
МОП	1101,22
С/у	127,66
Служеные помещения	854,95
Техническое помещение	244,11
Читальная зона	991,17

						1234 - ЭП-1	
						Многоквартирный жилой комплекс: «Многоквартирный жилой комплекс со встроенными помещениями и паркингом, III очередь строительства»	
Изм.	Кол.уч.	Лист	№док.	Подп.	Дата		
		Иванов А.				Стадия	Лист	Листов
						РП	0-2	
						Отделочный план 1го этажа Библиотеки на отм. 0,000	Лого	

Взам. инв. №

Подп. и дата

Инв. № подл.

02.11.2026 14:56:11

Формат А2А

Отделочный план 2го этажа Библиотеки на отм. +6.300



Условные обозначения

+7.500	-отметка уровня
1t	-марка пола
Д11	-марка двери
ОК-1	-марка окна
ПД-1	- подоконная доска
ВВ-1	- марка витража
холл	- наименование помещения
12.30	- площадь помещения

- Монолитный железобетон
- Керамический кирпич
- Газоблок
- Утеплитель



Количество комнат

- МОП
- С/у
- Служеные помещения
- Техническое помещение
- Читальная зона

Экспликация помещений 2го этажа...

Арендатор	Площадь
МОП	1042,52
С/у	93,47
Служеные помещения	434,85
Техническое помещение	215,76
Читальная зона	1843,71

Изм.	Кол.уч.	Лист	№док.	Подп.	Дата	1234 - ЭП-1		
		Иванов А.				Многоквартирный жилой комплекс: «Многоквартирный жилой комплекс со встроенными помещениями и паркингом, III очередь строительства»		
							Стадия	Лист	Листов
							РП	0-3	
						Отделочный план 2го этажа Библиотеки на отм. +6.300		Лого	

Взам. инв. №

Подп. и дата

Инв. № подл.

02.11.2026 14:56:12

Формат А2А


Отделочный план 3го этажа Библиотеки на отм. +11.100



Условные обозначения

+7.500	-отметка уровня
1т	-марка пола
Д11	-марка двери
ОК-1	-марка окна
ПД-1	- подоконная доска
ВВ-1	- марка витража
холл	- наименование помещения
12.30	- площадь помещения

- Монолитный железобетон
- Керамический кирпич
- Газоблок
- Утеплитель

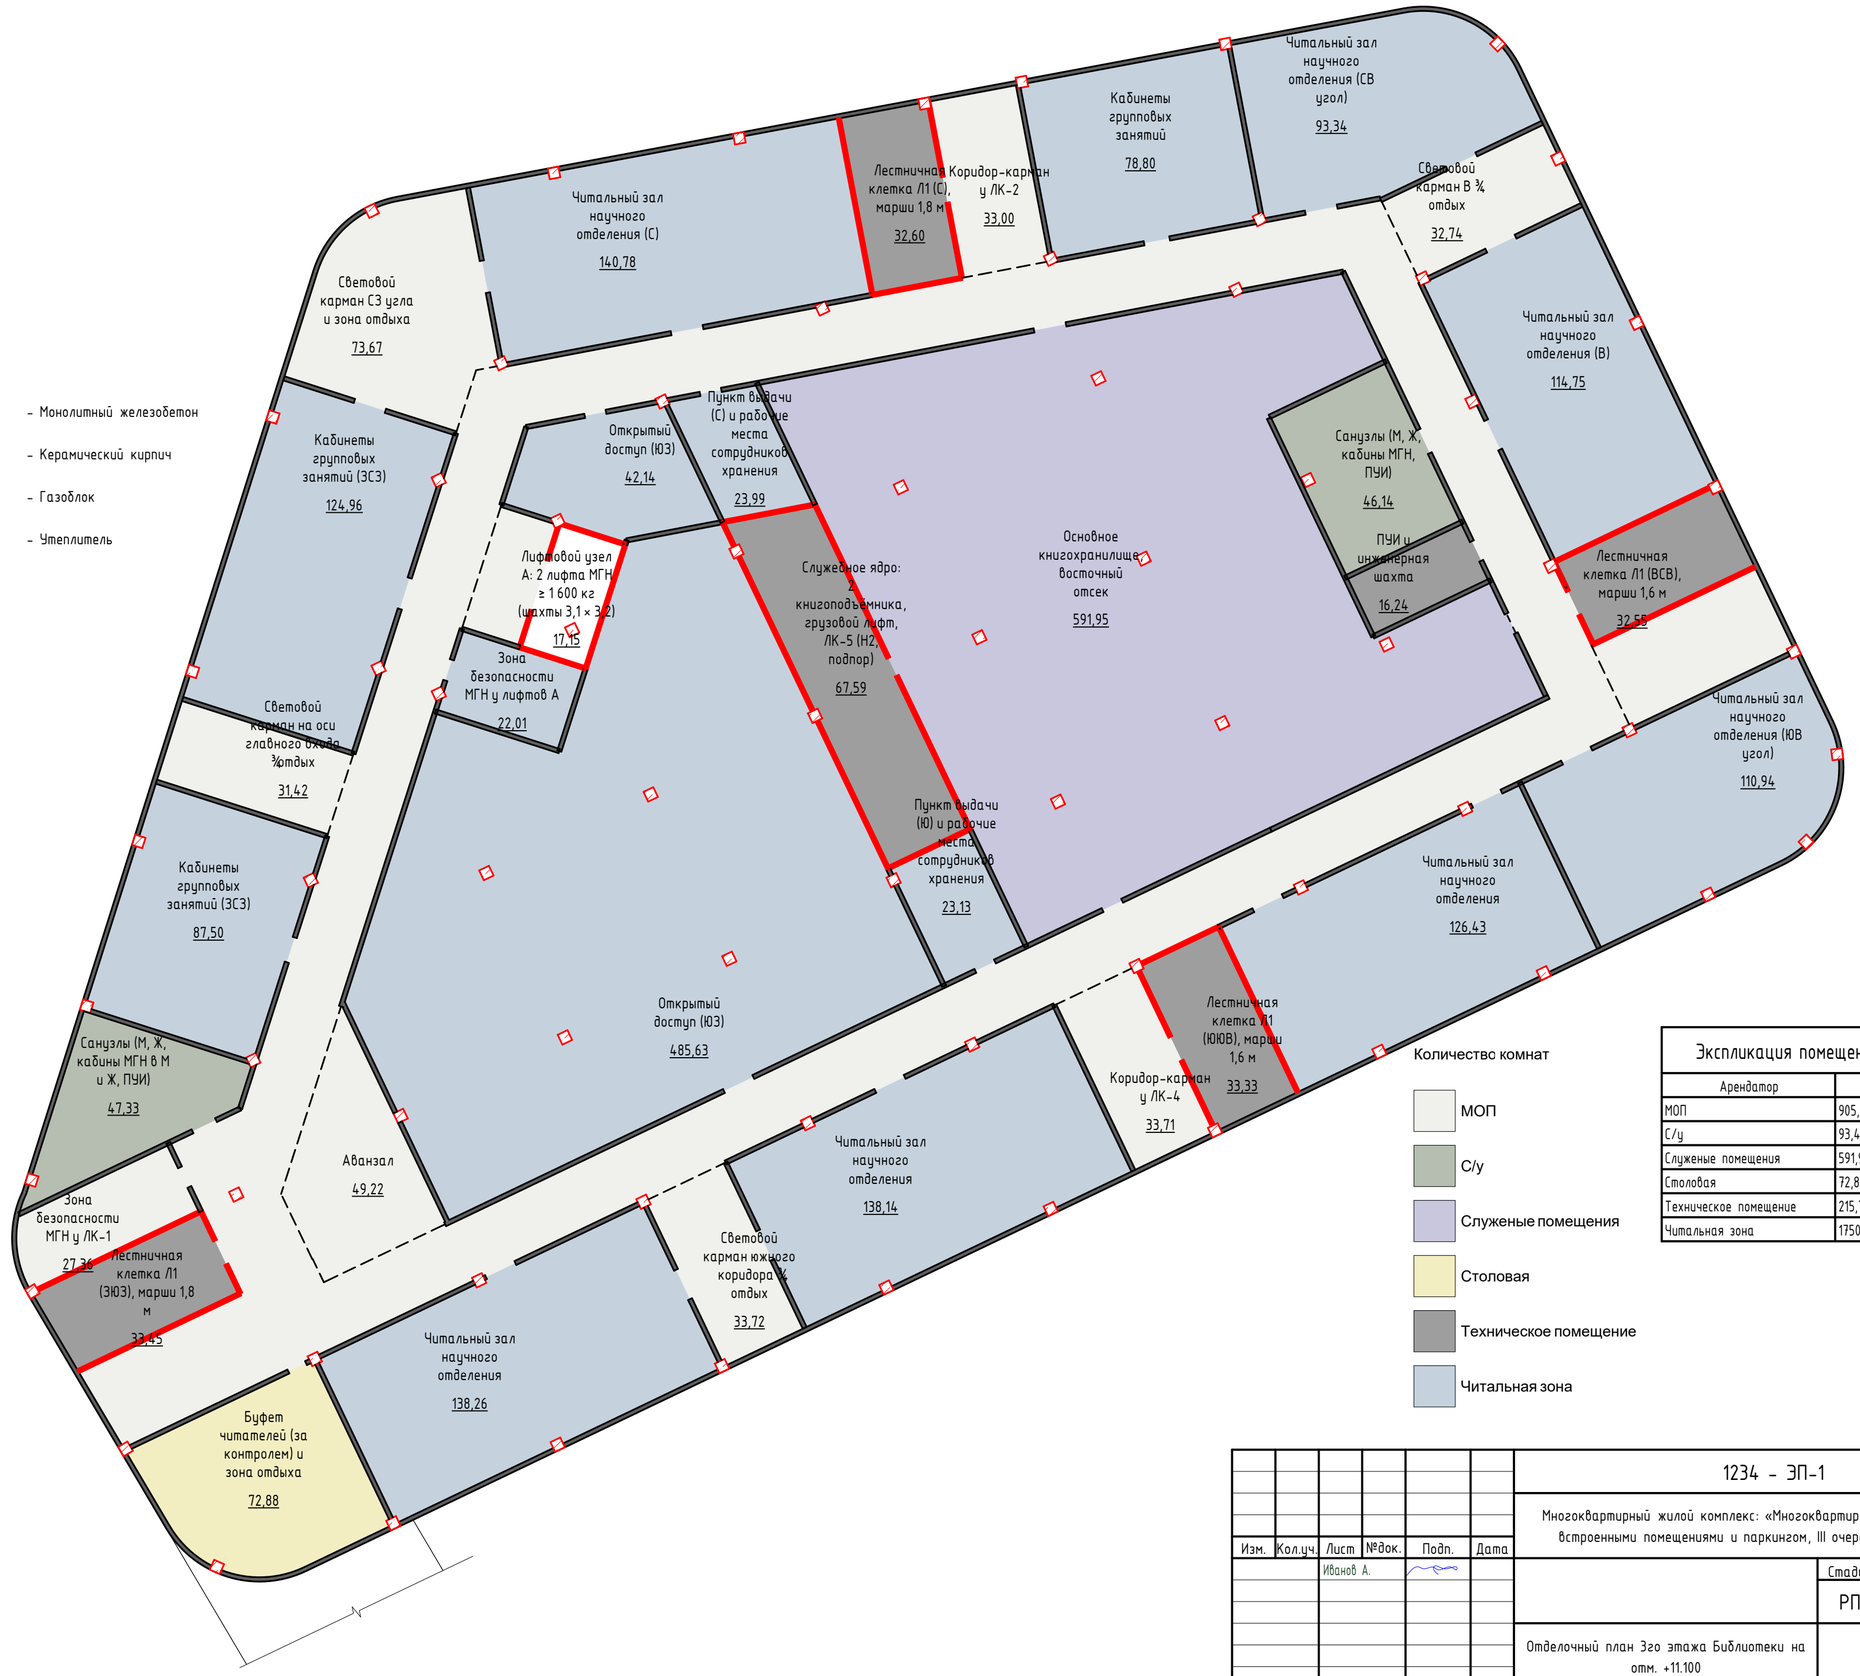

Количество комнат

- МОП
- С/у
- Служеные помещения
- Столовая
- Техническое помещение
- Читальная зона

Экспликация помещений 3го этажа...

Арендатор	Площадь
МОП	905,10
С/у	93,47
Служеные помещения	591,95
Столовая	72,88
Техническое помещение	215,76
Читальная зона	1750,82

Изм.	Кол.уч.	Лист	№док.	Подп.	Дата	1234 - ЭП-1		
		Иванов А.				Многоквартирный жилой комплекс: «Многоквартирный жилой комплекс со встроенными помещениями и паркингом, III очередь строительства»		
							Стадия	Лист	Листов
							РП	0-4	
						Отделочный план 3го этажа Библиотеки на отм. +11.100	Лого		

Взам. инв. №

Подп. и дата

Инв. № подл.

02.11.2026 14:56:13

Формат А2А

Отделочный план 4го этажа Библиотеки на отм. +15.900



Условные обозначения

+7.500	-отметка уровня	- Монолитный железобетон
1t	-марка пола	- Керамический кирпич
Д11	-марка двери	- Газоблок
ОК-1	-марка окна	- Утеплитель
ПД-1	- подоконная доска	
ВВ-1	- марка витража	
холл	- наименование помещения	
12.30	- площадь помещения	



Количество комнат

- МОП
- С/у
- Служеные помещения
- Техническое помещение
- Читальная зона

Экспликация помещений 3го этажа...

Арендатор	Площадь
МОП	905,10
С/у	93,47
Служеные помещения	591,95
Столовая	72,88
Техническое помещение	215,76
Читальная зона	1750,82

Изм.	Кол.уч.	Лист	№док.	Подп.	Дата	1234 - ЭП-1		
		Иванов А.				Многоквартирный жилой комплекс: «Многоквартирный жилой комплекс со встроенными помещениями и паркингом, III очередь строительства»		
							Стадия	Лист	Листов
							РП	0-5	
						Отделочный план 4го этажа Библиотеки на отм. +15.900	Лого		

Взам. инв. №
Подп. и дата
Инв. № подл.

02.11.2026 14:56:14

Формат А2А